18505-U

DISPOSICION Nº 110– ART. 2g)

"EL PRESENTE PLANO DE MENSURA SE REGISTRA AL SOLO Y UNICO EFECTO DE APORTAR AL JUEZ QUE ENTENDERA EN EL EVENTUAL JUICIO DE USUCAPION LOS ELEMENTOS DE LA PARCELA QUE DICE SER POSEÍDA, AL MOMENTO DE REALIZARSE LAS OPERACIONES DE MENSURA, NO PUDIENDO POR LO TANTO SERVIR DE BASE PARA LA TRANSFERENCIA DE DOMINIO, PREVIA SENTENCIA JUDICIAL".

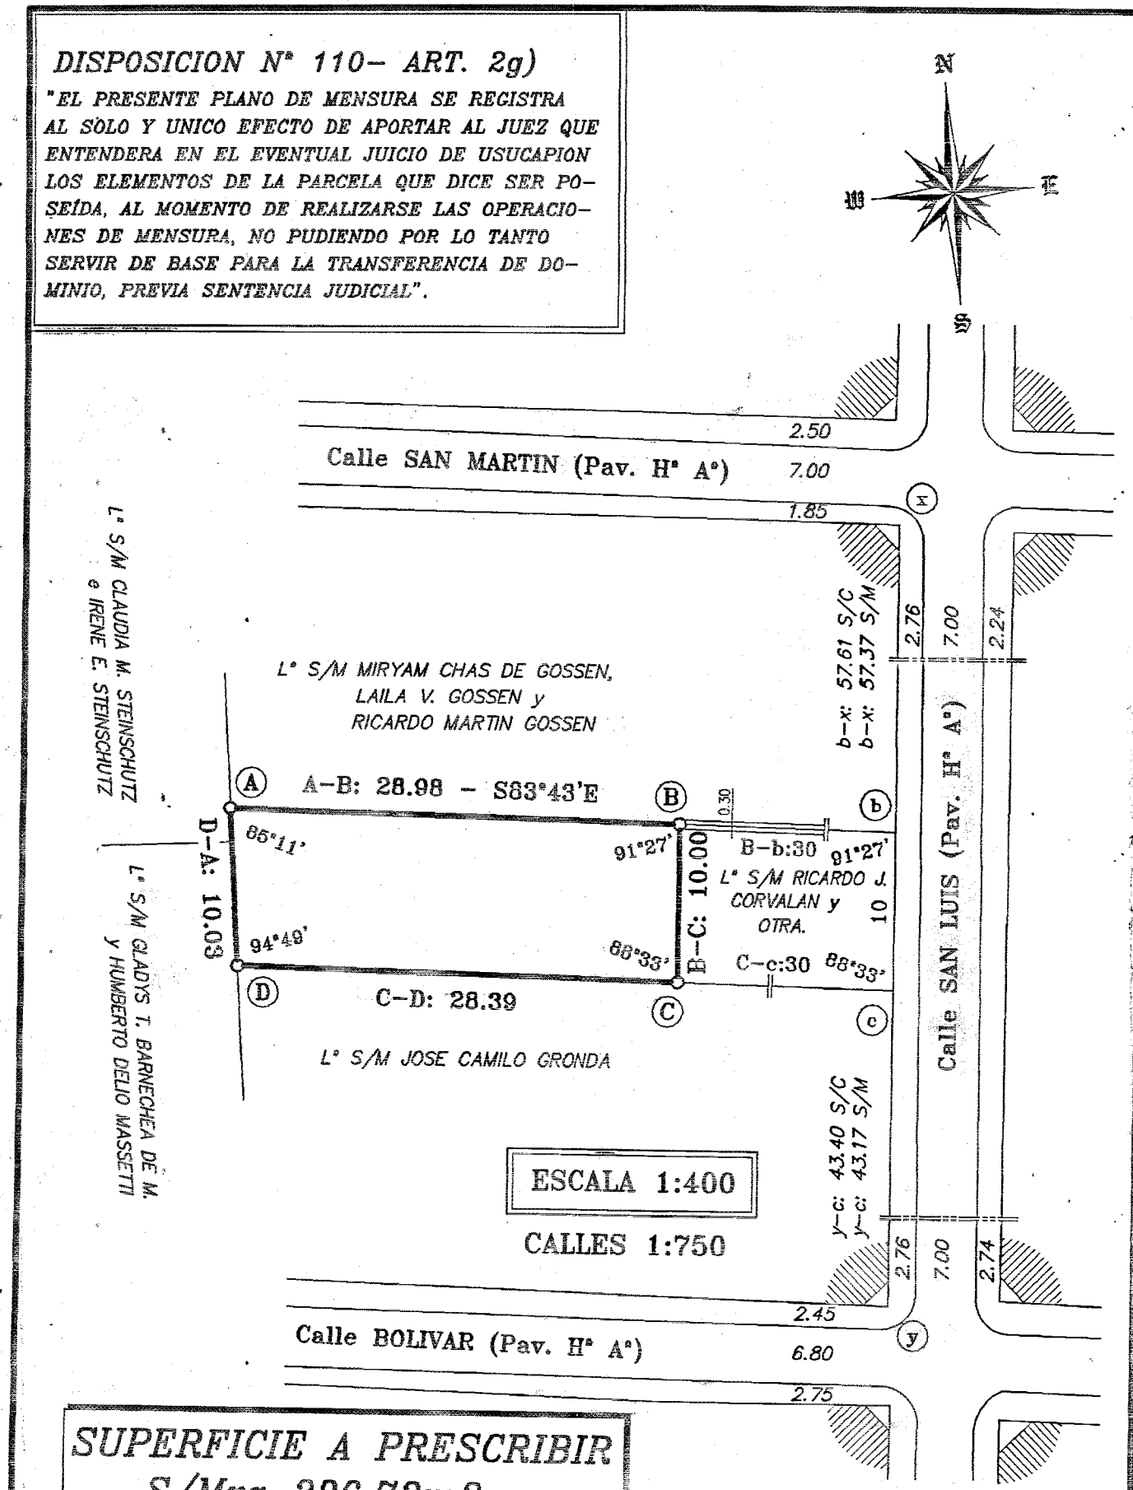

SUPERFICIE A PRESCRIBIR
S/Mra 286,73m2

NOTAS:

- Las medidas lineales están expresadas en metros.
- Rumbo adoptado del lado (B–C): N83°43'O Mra. 10665–U, para el lado (A–B) de estas operaciones.
- Estas operaciones se superponen al polígono a–D–C–b–a, de la Mensura 10665–U.
- Estas operaciones se superponen parcialmente a la Mra. 2452–U.
- Los poseedores del inmueble objeto del presente trabajo acceden a la vía pública a través del inmueble que limita al Este, cuyo dominio les pertenece, y queda acreditado según informe del Registro de la Propiedad Inmueble que adjunto al expediente.

REFERENCIAS:

- Muros.
- Linea de mensura.
- Mojón de madera colocado.
- Edificación existente
- S/M Según Mensura.
- S/C Según Catastro.

Objeto: MENSURA PARA PRESCRIPCION ADQUISITIVA

Mensura Nº 18505-U

Nomenclatura Catastral

Carácter: Particular

Provincia de Corrientes – República Argentina

Departamento: CAPITAL.

Lugar: Planta Urbana de la Ciudad de Corrientes.

Posesión de:

Ricardo Jorge CORVALAN y María Emilia del Pilar GRONDA

Ubicación: Manzana Nº 239, Parcela Nº 40, Bº "CAMBA CUA"

PARTIDA INMOBILIARIA: A1–2094–1

PROPIEDAD DE: LA PIA UNION DE SAN ANTONIO DE PADUA. (IGLESIA DE SAN FRANCISCO).

Dominio: Insc. Reg. Prop. Pcia.: Tº 401, Fº 116.529 vto., Fca. 1639, Año 1937.
Insc. Reg. Prop. Mpal.: NO SE ENCONTRO.

PARTIDA INMOBILIARIA: A1–2094–1.

Mensuras Relacionadas: 2452–U; 3140–U; 10665–U.

APROBADO EXCLUSIVAMENTE EN EL ASPECTO GEOMETRICO

CROQUIS DE UBICACION

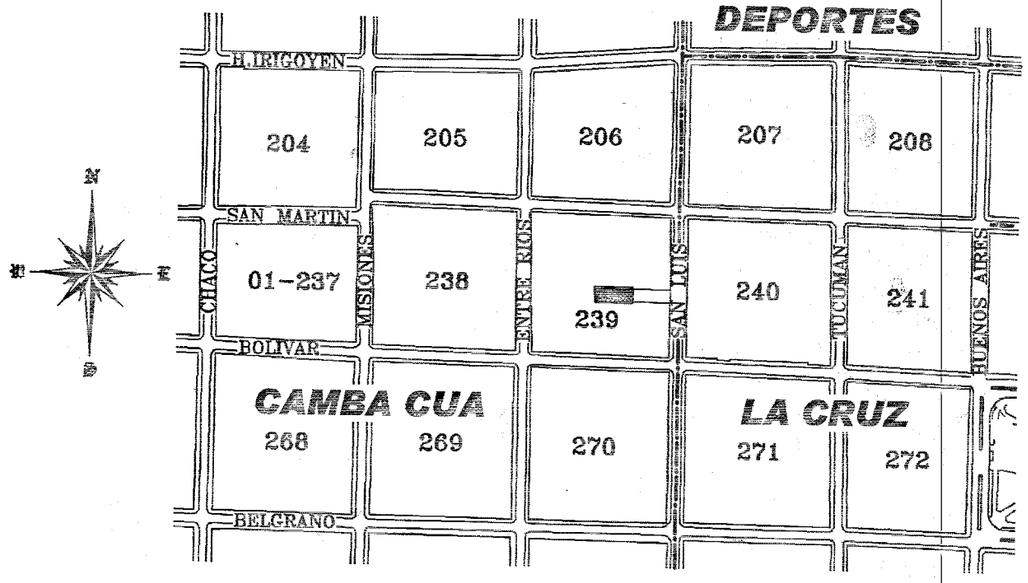

Corrientes, Capital, 10 de Febrero de 2006.

Los elementos consignados en el presente plano son de exclusiva responsabilidad del profesional actuante.

ALICIA CECILIA CANEVARO	RICARDO J. CORVALAN	MARIA E. del P. GRONDA
Agrimensor Nacional	POSEEDOR	POSEEDORA
M.C.P. 2049 – D.G.C. 750	DNI 13.579.731	DNI 16.357.480
Dom. Bolívar Nº 558 – Ctes.	Dom. San Luis Nº 1170 – Ctes.	Dom. San Luis Nº 1170 – Ctes.

DIG