**Referencias:**

- Mojòn de hierro encontrado.-
- Mojón de hierro colocado.-
- Linea de Mensura.-
- Edificación existente.-
- Muros existentes.-
- Muro bajo con rejas.-
- Columna de H° A°.-

**Notas:**

- Medidas lineales dadas en metros.-
- Rumbo Magnetico medido lado A-B=N-82°31'-O, del presente trabajo.-
- Calles: Escala 1 : 750.-
- Los vertices B; C y D, del presente trabajo estan perfectamente materializados con muros existentes.-
- La Linea Municipal se tomo teniendo en cuenta el mojon de H° encontrado en las esquinas de las Calles San Luis e Hirigoyen, con la edificacion existente sobre calle objeto del presente trabajo.-

**Balance de Superficies**

| | |
|---|---|
| Sup. S/Titulo (Calculada) | 333,50 m2 |
| Sup. S/Mensura | 334,72 m2 |
| Diferencia en (+) | 1,22 m2 |

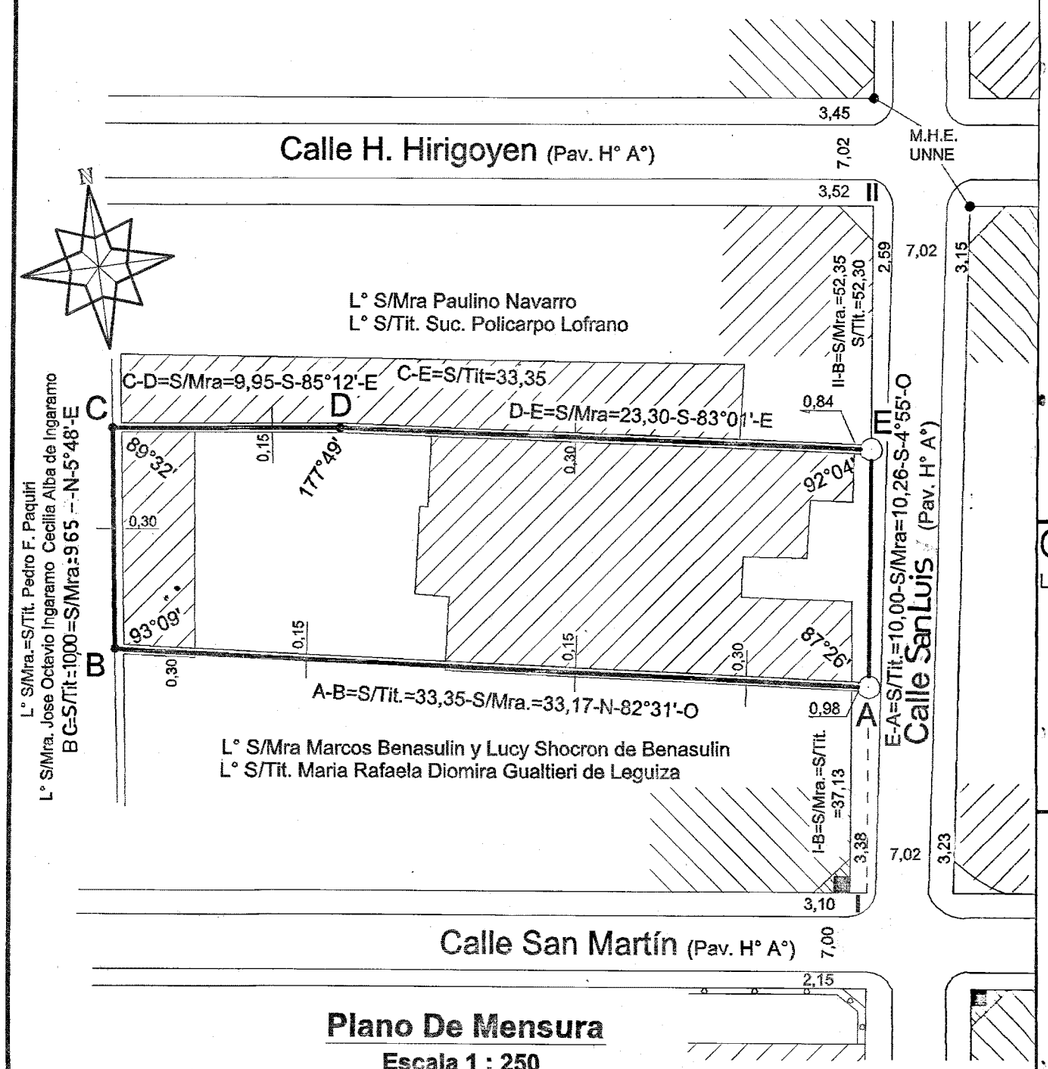


**Plano De Mensura**

**Escala 1 : 250**

Objeto: **Mensura .-**

Caracter: **P a r t i c u l a r .-**

Provincia De **CORRIENTES** - Rep. Argentina.-

Departamento: **C a p i t a l .-**

Lugar: **Ciudad de Corrientes.-**

Mensura Nº 17.766-U

Nomenclatura Catastral

Propietario:

***Isabel Marta GARCIA NAVARRETE***

Ubicaciòn: **Manz. N° 206 - Lote N° 5 S/Tit. y Lote N° 18 - S/Cat "B° Camba Cua".-**

Dominio: **Reg. Prop. Prov.**: F° Real Mat. N°10.245 - Año 1.981.-

Reg. Prop. Munic.: L°4 - T° 24 - N° 356 - F° 388 - Año 1.981.-

Adrema: **A1 - 4.571 - 1.-**

Mensuras Relacionadas: 3.715-U.-

Croquis de Ubicaciòn:

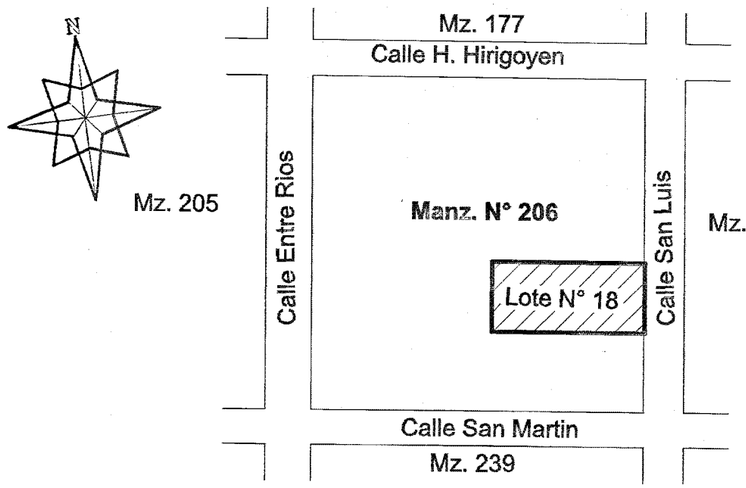


Corrientes; Capital; 22 de Septiembre de 2.004.-

Los elementos consignados en el presente expediente son de exclusiva responsabilidad del profesional actuante.-

EDUARDO ZIBECCHI
Agrimensor Nacional
C.P.Nº 2.458 - D.G.C.Nº 814
Calle Sicilia N° 5.030 - Ctes.-

ISABEL MARTA GARCIA NAVARRETE
Propietaria
D.N.I. N° 12.440.682
Dom.: San Luis N° 1.074 - Ctes.