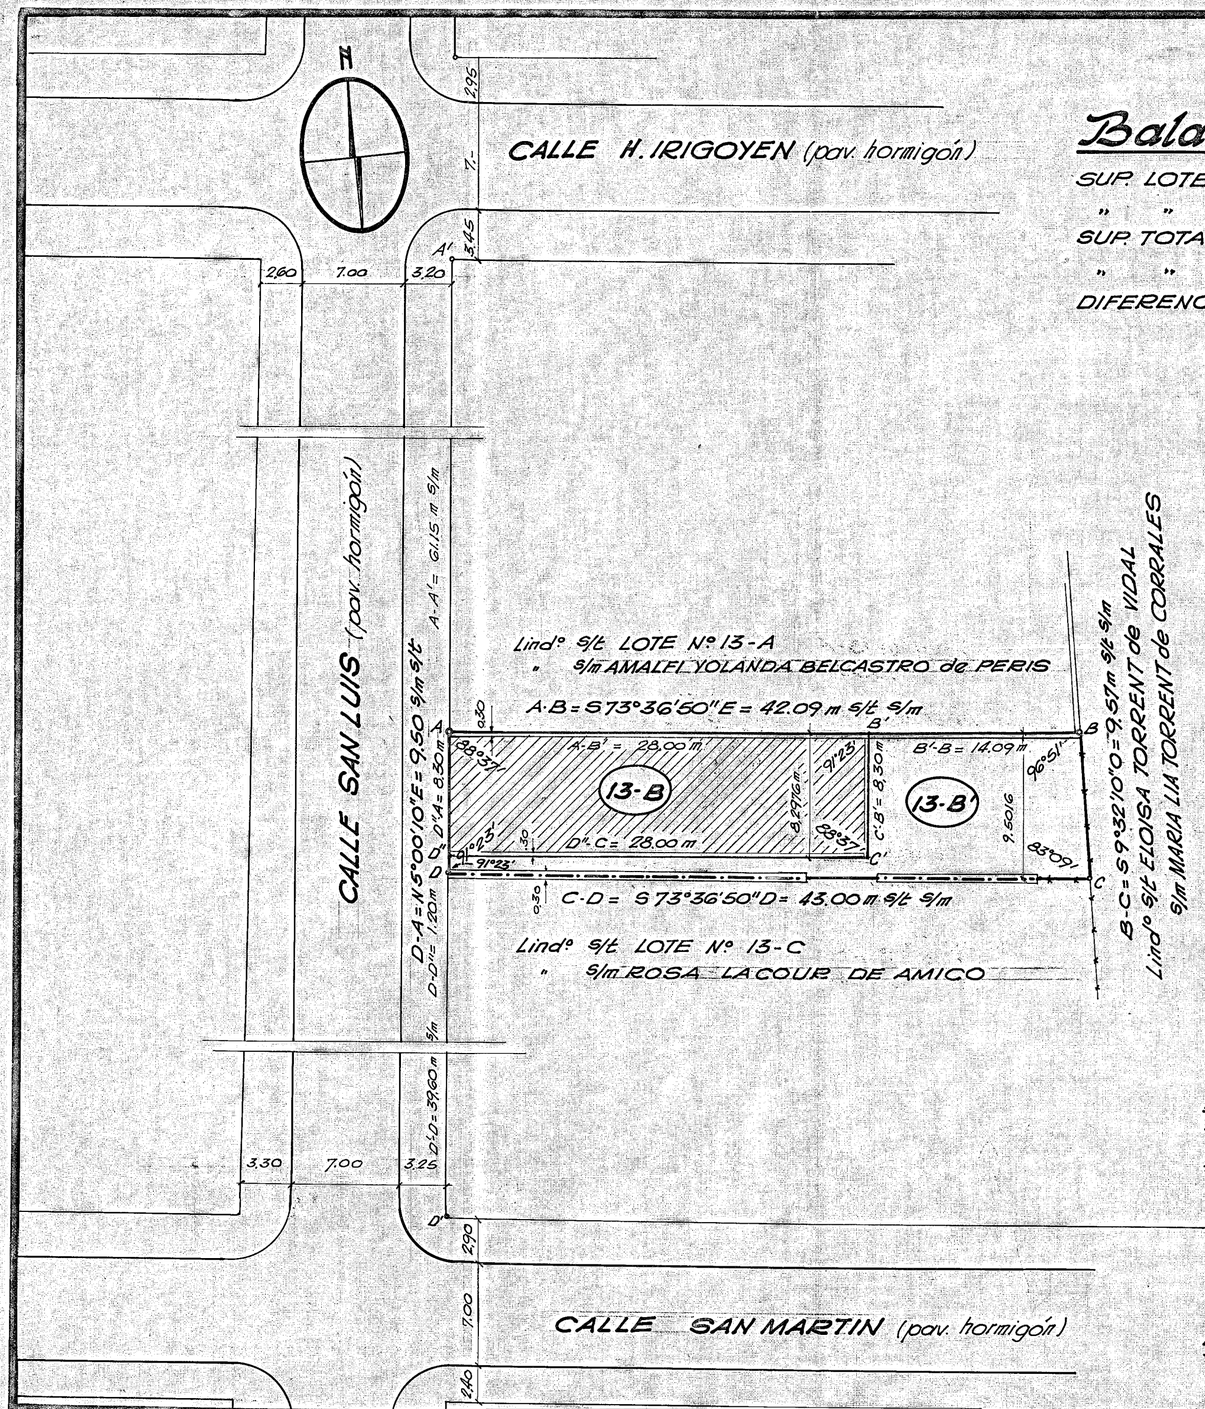

Balance de Superficies

SUP. LOTE 13-B	=	232,3328	m²
" " 13-B'	=	171,7820	"
SUP. TOTAL s/m	=	404,1148	m²
" " s/t	=	404,1973	"
DIFERENCIA EN (-)	=	0,0825	m²

NOTAS
* Los angulos no consignados son suplementarios
* Rumbo adoptado del Dup. N° 2825 "U"

OBJETO: REMENSURA Y DIVISION DEL LOTE 13 DEL DUPLICADO 2232 "U"
CARACTER: PARTICULAR
PROVINCIA DE CORRIENTES - REP. ARGENTINA
DEPARTAMENTO: CAPITAL
LUGAR: MUNICIPIO DE CORRIENTES

DUP. DE MENSURA: 3356-U
NOMENC. CATASTRAL:

PROP. DE Carlos Lorenzo GONZALEZ

UBICACION: MANZANA N° 207 - LOTE N° 13-B
Calle: San Luis entre H. Irigoyen y S. Martín

DOMINIO:
REG. DE LA PROP. DPTO. CAPITAL
N° 1033 - F° 1157 - T° 5° (10-IX-68)
REG. DE LA PROP. MUNICIPAL
F° 1281 - Finca 1227 - T 7° - L 4° - (26-IX-68)
ADREMA A1 - 16.979-1 (20-IX-68)

12

CROQUIS DE UBICACION

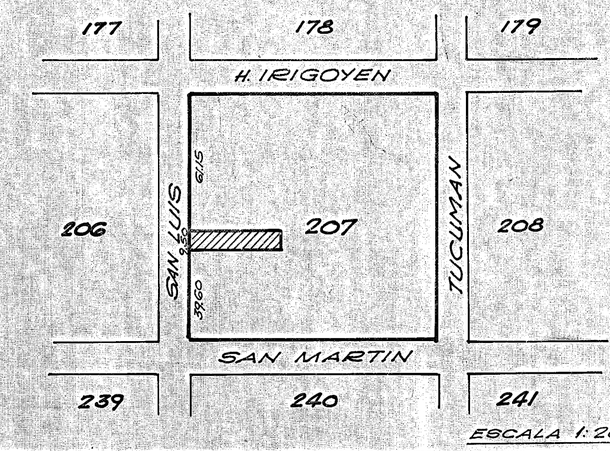

CORRIENTES, 3 DE NOVIEMBRE DE 1970

DARIO PEREZ	DANIEL QUIROZ	CARLOS LORENZO GONZALEZ
Agrimensor Nacional	Agrimensor Nacional	Propietario
C.P.N° 392 - Matr. N° 316	C.P.N° 350 - Matr. 297	M.I. N° 5.627.267
Av. Maipú 787	Rep. del Líbano 296	